As per Rule No.TPS 1816/ CR-386(Part-I)/ 15/37(1CC)G/ VI YO /UD-13: Dated 8th March, 2019. (INTEGRATED TOWNSHIP PROJECT)

S.No.	AS PER RULE NO.	LAND USE DESCRIPTION	AS REQUIRED IN ITP		LAND AREA		LAND USE PERCENTAGE	MINIMUM REQUIRED FSI	ALLOTTED BASIC FSI	SECTOR WISE BASIC FSI	BALANCE / PROPOSED BASIC FSI	ALLOTTED PREMIUM FSI	Sanctioned Premium	Balance Premium	Allotted Ancillary F.S.I	Sanctioned Sector Wise Ancillary	Balance Ancillary	TOTAL FSI (BASIC+ PREMIUM)	INDEX
	Master Layout Area (MLA) =	409061.53	As per Rule	As per ITP	SQ.M.	ACRES	%	SQ.M.	SQ.M.	SQ.M.	SQ.M.	SQ.M.						SQ.M.	
1	2	3	4	5	6	7	8	9	10.00	11	12	13						14.00	15
2	7.3 a (i)	Garden	MLA X 2.5 percent	10226.54	10307.76	2.58	2.52	0.00	0.00	0.00	0.00	0.00						0.00	0.00
3	7.3 a (ii)	Playground	MLA X 7.5 percent	30679.61	31229.24	7.81	7.63	0.00	0.00	0.00	0.00	0.00						0.00	0.00
4	7.3 a (iii)	Garden on hiilslope	MLA X 2.5 percent	10226.54	21402.83	5.35	5.23	0.00	0.00	0.00	0.00	0.00						0.00	0.00
5		Garden on slope less than 1:5			30950.85	7.74	7.57	0.00	0.00	0.00	0.00	0.00						0.00	0.00
6	7.3, b	Primary & Secondary School	Req. for40 Ha.Req.Min.plot = 5000	FOR 41.90 HA = 5237.5	5120.87	1.28	1.25	0.00	5500.00	0.00	5500.00	4500.00	0.00	0.00	0.00	0.00	0.00	10000.00	1.95
7	7.3 c	Community Health Care Facilities	Req. for40 Ha.Req.Min.plot = 1000	FOR 41.90 HA = 1047.5	3053.87	0.76	0.75	1500.00	40906.36	0.00	40906.36	0.00	0.00	0.00	0.00	0.00	0.00	40906.36	13.39
8	7.3 d	Public Assembly Facilities	5000sq.m. land	5000	5350.39	1.34	1.31	5000.00	5400.00	0.00	5400.00	0.00	0.00	0.00	0.00	0.00	0.00	5400.00	1.01
9	7.3 f	Public Utilities	As per norms		10483.46	2.62	2.56	0.00	0.00	0.00	0.00	0.00						0.00	0.00
10	7.3 g	Transport & Communication	As per norms		77811.63	19.45	19.02	0.00	0.00	0.00	0.00	0.00						0.00	0.00
11	7.4	Residential	Min. 60% FSI of Total Proposed Basic FSI		261738.14	65.43	63.99	245436.92	357255.17	108695.65	248559.52	404561.53	0.00	0.00	490873.836	0.00	0.00	1252690.54	4.79
12	7.5	Open Space(10%)			10910.94	2.73	2.67	0.00	0.00	0.00	0.00	0.00						0.00	0.00
13	8	Share of Local/Planning Authority	2 percent	8181.23	8679.02	2.17	2.12	0.00	0.00	0.00	0.00	0.00						0.00	0.00
		GRAND TOTAL	0.00	409061.53	477039.00	119.26	116.62	409061.53	409061.53	108695.65	300542.88	409061.53						1308996.90	2.74

SOCIAL HOUSING CALCULATIONS

MLA	RESI. FSI FOR CONSIDERED FOR SOCIAL HOUSING	PERCENTAGE	AREA REQUIRED FOR SOCIAL HOUSING (SQ.M.)
409061.53	245436.918	15%	36815.54
LIG		75%	27611.65
EWS		25%	9203.88

FOR SECTOR -R3 PLOTTED LAYOUT

TABLE NO. 12 FOR SECTOR R4 PLOTTED LAYOUT

SECTOR -R5 PLOTTED LAYOUT

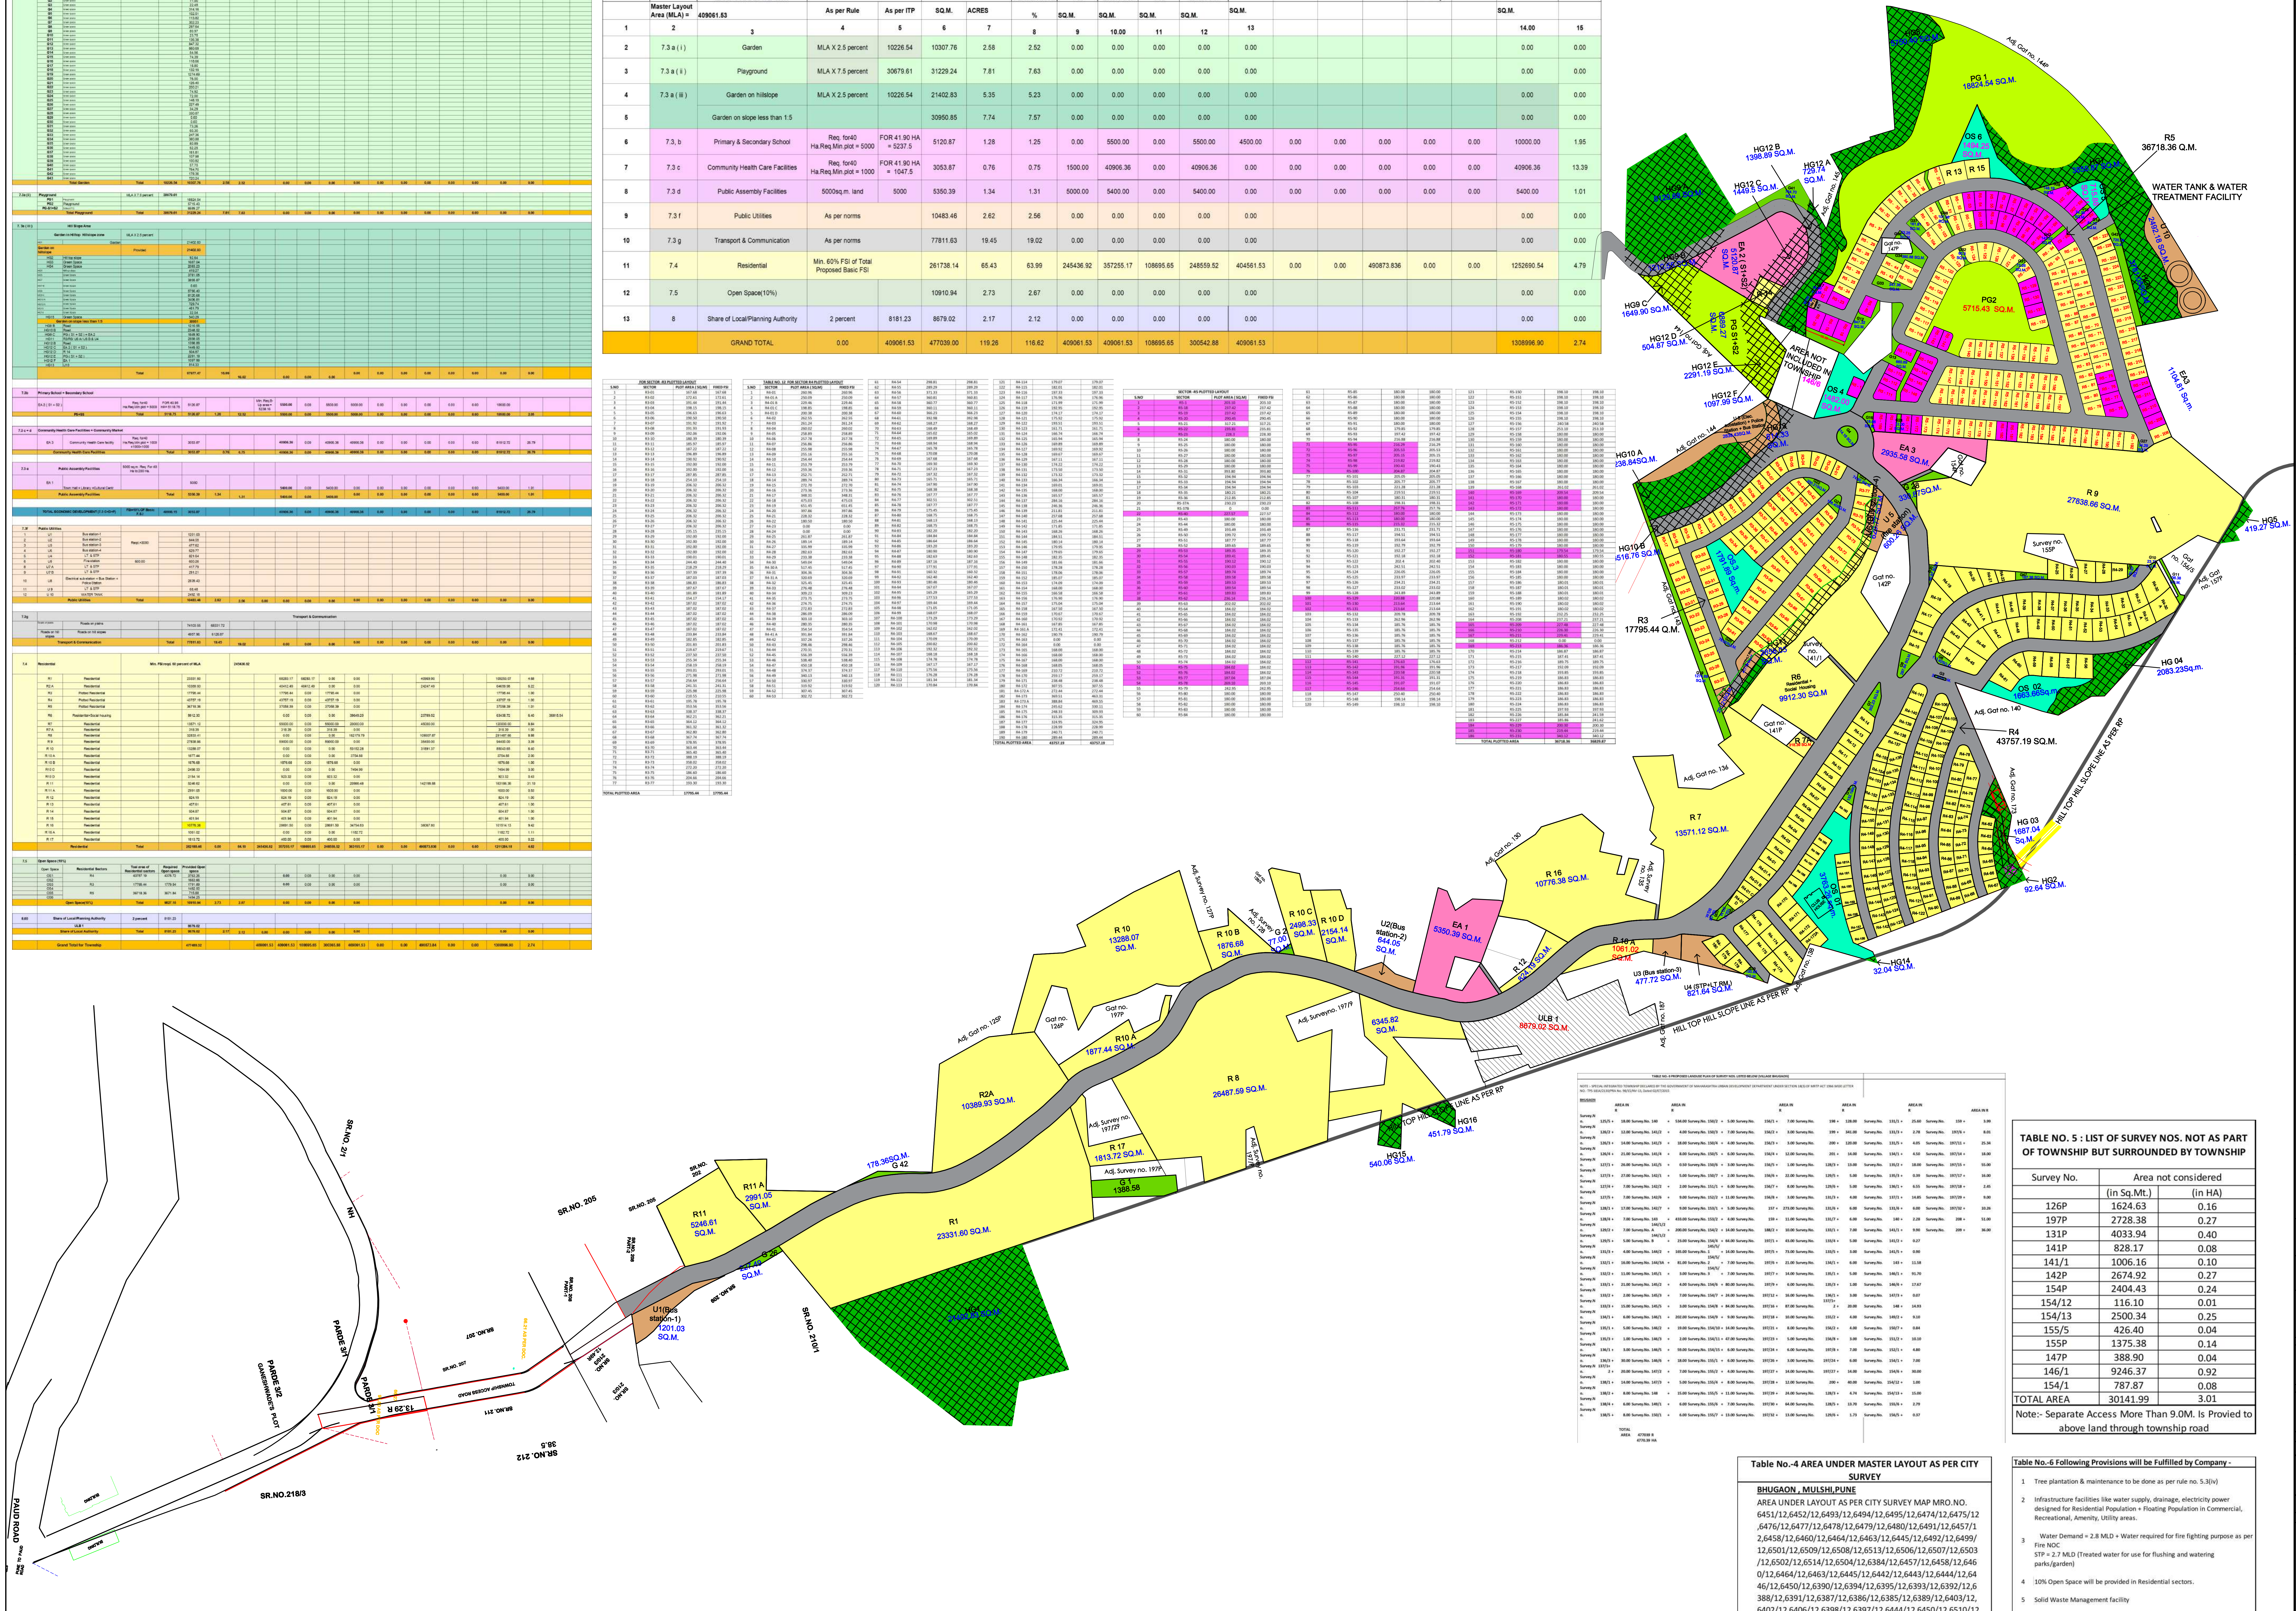

TABLE NO.-3 PROPOSED LANDUSE PLAN OF SURVEY NOS. LISTED BELOW (VILLAGE BHUGAON)

NOTE :- SPECIAL INTEGRATED TOWNSHIP DECLARED BY THE GOVERNMENT OF MAHARASHTRA URBAN DEVELOPMENT DEPARTMENT UNDER SECTION 18(5) OF MRTP ACT 1966 WIDE LETTER NO.- TPS-1814/2130/PRA No. 98/15/NV-13, Dated 02/07/2015

BHUGAON

STAMP OF APPROVAL OF PLANS

3/3

Approved as amended in

Subject to conditions mentioned in Annexure "A" of letter

No. BMU / C.R. No. 2092/23-24 / Mouza भुगाव /

S. No. / G. No. / CTS No. १२४/४ , १२६/२ वगैरे

Dated :- 23 09 /2024

Deputy / Joint Metropolitan planner

Pune Metropolitan Regional Development Authority, Pune

S.No.		PREVIOUS SANCTION AS PER PLU 12-07-24	AREA IN HA.	TOTAL PROPOSED ITP	AREA IN HA.	AREA IN ACRES
1	PLOT AREA	419034	41.9	477039	47.7	117.88
2	AREA UNDER TOWNSHIP	419034	41.9	477039	47.7	117.88
3	TOTAL HILLSLOPE AREA	66985.62	6.7	67977.47	6.8	16.80
4	AREA UNDER DEVELOPMENT FOR CALCULATION OF FSI AND AMENITIES	419034	41.9	409061.53	40.9	101.08
5	BASIC FSI POTENTIAL OF TOWNSHIP	419034	41.9	409061.53	40.9	101.08
6	PREMIUM FSI POTENTIAL	293323.8	29.3	409061.53	40.9	101.08
7	Ancillary F.S.I	NA	NA	490873.836	49.1	121.30
8	TOTAL FSI	712357.8	71.2	1308996.896	130.9	323.46

TABLE NO. 1

TABLE NO.-2 DETAILS OF ALL NOC'S AND APPLICABLE RULES

INTEGRATED TOWNSHIP POLICY APPICABLE :- As per Rule No.TPS 1816/ CR-368(Part-I)/ 15/37(1CC)G /VI YO/ UD-13: Dated 8th March, 2019. (INTEGRATED TOWNSHIP PROJECT)

PREVIOUS SANCTIONED UNDER SPECIAL TOWNSHIP RULES
Special Township under regulation sanctioned by Govt. Notification TPS-1812/953/R.P. PUNE/CR-184/12/20(4)/UD-13 of MRTP Act 1966 regarding developement of Township in area under Pune RP on - 30/05/2014

LOCATIONAL CLEARANCE
Goverment Notice No. TPS-1814/2130/PRA No. 98/15/NV-13, Dated 02/07/2015 Notified land - 41.9034 Hectares

LETTER OF INTENT
Letter of intent given by Colletctor Pune vide Letter No.MULSHI/NA/SR/07/2018, Dated 02/02/2018

ENVIRONMENTAL CLEARANCE (NOC)
The Environmental Clearance Granted by Ministry of Environment, Forest & Climet Change vide Letter No. 21-52/2017-IA-III, dated on 10/08/2017
Amendment in EC Granted by Environmental depatment, Letter no.SEIAA Cell/CR-137-2018,dated on 30/11/2018

WATER SUPPLY (NOC)
Noc From Maharashtra Krushana Khore Vikas Mahamandal, Pune, Vide Letter No.- MU.A./KAA-2/PRASHA-6/VINAM/(241/23)/6240/SAN 2015, dated on 29/12/2015

BURIAL AND CREMATION GROUND (NOC)
Noc from Grampanchayat Bhugaon for Burial & Cremation Ground, Vide Letter No. 253/18, dated on 09/03/2018

ELECTRICITY SUPPLY (NOC)
Letter from Chief Engineer, MSEDCL, Pune Zone, Pune
Letter No.- KAA/MULSHI/TA/NO 278, dated on 11/01/2013

ARCHOLOGICAL DEPARMENT (NOC)
Letter From Director of Archiological Deparment Gov.of Maharashtra Vide Letter No.- TANTRA/NAHARAKAT/2014/2105, dated on 03/09/2014

FOREST DEPARMENT (NOC)
Letter from Forest Officer Mulshi Vide Letter No.- A/IAMIN/38/373/SAN 12-13, dated on 08/01/2013

MINISTRY OF DEFENCE(NOC)
Letter from Ministry of defence of India,Gandhinagar, Gujrat-Letter no-SWAC/2564/6/2586/ATS(8M),dated on 29/04/2021
Letter from ATS,Air headquarters ,Delhi-Letter no-Air HQ/S 17726/4/1/ATS(PC-MMMCXLI) ,dated on 20/05/2021

LEGEND	
PROJECT BOUNDARY	▭
SECTOR BOUNDARY	▭
EXISTING ROAD	▭
PROPOSED R.P. ROAD	▭
PROPOSED INTERNAL ROADS	▭
GREEN SPACE	■
RESIDENTIAL	■
AMENITY	■
UTILITY	■
COMMERCIAL	■
AREA NOT INCLUDED IN SCHEME	▨
HILLTOP HILLSLOPE AREA	▦
OPEN SPACE AREA	■
PLAY GROUND	■
AFFORESTATION ZONE	▨
EXISTING STRUCTURES	▭

TABLE NO. 5 : LIST OF SURVEY NOS. NOT AS PART OF TOWNSHIP BUT SURROUNDED BY TOWNSHIP

Survey No.	Area not considered	
	(in Sq.Mt.)	(in HA)
126P	1624.63	0.16
197P	2728.38	0.27
131P	4033.94	0.40
141P	828.17	0.08
141/1	1006.16	0.10
142P	2674.92	0.27
154P	2404.43	0.24
154/12	116.10	0.01
154/13	2500.34	0.25
155/5	426.40	0.04
155P	1375.38	0.14
147P	388.90	0.04
146/1	9246.37	0.92
154/1	787.87	0.08
TOTAL AREA	30141.99	3.01

Note:- Separate Access More Than 9.0M. Is Provied to above land through township road

Table No.-4 AREA UNDER MASTER LAYOUT AS PER CITY SURVEY

BHUGAON , MULSHI,PUNE

AREA UNDER LAYOUT AS PER CITY SURVEY MAP MRO.NO. 6451/12,6452/12,6493/12,6494/12,6495/12,6474/12,6475/12,6476/12,6477/12,6478/12,6479/12,6480/12,6491/12,6457/12,6458/12,6460/12,6464/12,6463/12,6445/12,6492/12,6499/12,6501/12,6509/12,6508/12,6513/12,6506/12,6507/12,6503/12,6502/12,6514/12,6504/12,6384/12,6457/12,6458/12,6460/12,6464/12,6463/12,6445/12,6442/12,6443/12,6444/12,6446/12,6450/12,6390/12,6394/12,6395/12,6393/12,6392/12,6388/12,6391/12,6387/12,6386/12,6385/12,6389/12,6403/12,6402/12,6406/12,6398/12,6397/12,6444/12,6450/12,6510/12,6512/12,6511/12 DATE 31/03/2012

Table No.-6 Following Provisions will be Fulfilled by Company -

1 Tree plantation & maintenance to be done as per rule no. 5.3(iv)

2 Infrastructure facilities like water supply, drainage, electricity power designed for Residential Population + Floating Population in Commercial, Recreational, Amenity, Utility areas.

3 Water Demand = 2.8 MLD + Water required for fire fighting purpose as per Fire NOC
STP = 2.7 MLD (Treated water for use for flushing and watering parks/garden)

4 10% Open Space will be provided in Residential sectors.

5 Solid Waste Management facility

6 Decentralized Sewage Treatment Plant to be provided as per requirement.

PROPOSED MASTER LAYOUT PLAN (PLU) OF
M/s. KALEIDOSCOPE DEVELOPERS PVT. LTD. AT
VILLAGE- BHUGAON, TAL.- MULSHI, DIST.- PUNE

NOTE -
1:- THIS DRAWING IS BASED ON IN PERMISSION AND DOCNUMENT PROVIDED BY OWNER/P.A.H.
ARCHITECT WILL NOT BE RESPONCIBLE FOR ANY DISPUTE DIFFRENECES OR ANY LEGALITY OF THE OWNERSHIP.

2 :- THIS DRAWING IS COPY RIGHT OF ARCHISTRUCTURE CONSALTANCY & THIS DRAWING SHOULD NOT BE COPIED OR USED WITHOUT PRIOR PERMISSION OF THE ARCHITECT

CERTIFICATE OF AREA

CERTIFIED THAT THE LAND UNDER REFERENCE LAYOUT WAS SURVEYED BY ME AND THE DIMENSIONS OF THE SITES ETC. OF PLOT STATED ON PLAN ARE MEASURED ON SITE AND THE AREA SO WORKED OUT TALLIES WITH THE AREA STATED IN MASTER PLAN DOCUMENT OF OWNERSHIP / CITY SURVEY RECORS AND MEASUREMENT PLAN.

SIGNATURE OF ARCHITECT

NAME OF OWNER / DEVELOPER

M/s. KALEIDOSCOPE DEVELOPERS PVT. LTD.

MR. SARANG SUDHAKAR KALE
(OWNER/P.O.A.)

NAME OF ARCHITECT

SCALE - 1: 2500	DATE - 26 OCT 2024	PROJECT ARCHITECT - AR.ARCHANA

NORTH

AR. SAMBHAJI D. PATIL

FILE PATH

ARCHLAND
ARCHITECTS PVT.LTD.

Ar.Sambhaji Patil

CTSNo.1108,Final Plot No.487,Sub Plot No.4,8-Manasara,
III Floor,T.P.Scheme No.1,GaneshKhind Road,
Shivajinagar,Pune-400 116

Tel: (020)25665859 Mob:098230 57750

Web:www.archlandindia.com
Email:myarchland@gmail.com,arsambhajipatil@gmail.com
arsambhajipatil@archlandindia.com