# BEFORE AMALGAMATIONS FOR KALEIDOSCOPE TOWNSHIP (41.90 HA)

NOTE :- SPECIAL INTEGRATED TOWNSHIP DECLARED BY THE GOVERNMENT OF MAHARASHTRA URBAN DEVELOPMENT DEPARTMENT UNDER SECTION 18(3) OF MRTP ACT 1966 WIDE LETTER NO.- TPS-1814/2130/PRA No. 98/15/NV-13, Dated 02/07/2015

LC1-S.NO
125/5, 126/2, 126/3, 126/4, 127/1,127/3,127/4,127/5,128/1,128/4,129/2,
129/5,131/3,132/1,132/2,133/1,133/2,133/3,134/1,135/1,135/3,136/1,136/3,
137/1+2,138/1,138/2,138/4,138/5,140,141/2,141/3,141/4,141/5,142/1,142/2,
142/6,142/7,143,144/1/2A,144/1/2B,144/2,144/3A,145/1,145/2,145/3,145/5,146/1,
146/2,146/3,146/5,146/6,147/2,147/3,148,149/1,150/1,150/2,150/3,150/4,150/5,150/6,
150/7,151/1,152/2,153/1,153/2,154/2,154/4,145/5/1,154/5/2,154/5/3,154/6,154/7,154/8,
154/9,154/10,154/11,154/15,155/1,155/2,155/4,155/5,155/6,155/7,156/1,156/2,156/3,156/4,
156/5,156/6,156/7,156/8,157,159,188/2,197/1,197/5,197/6,197/7,197/9,197/12,197/16,197/18,
197/21,197/23,197/24,197/26,197/27,197/28,197/29,197/30,197/32,198,199,200,201,128/3,
129/5,129/6,131/3,131/6,131/7,133/1,134/4,133/5,134/1,135/1,135/3,136/1,137/1+2,155/2,156/2,
156/8,197/8,197/24,197/27,200,

LC2 -NEW AREA ADDED
S.NO-128/3,129/5,129/6,131/1,131/3,131/5,134/1,135/2,135/3,136/1,
137/1,140,141/1,141/2,141/5,143,146/1,146/6,147/3,148,149/2,
150/7,151/2,152/1,154/1,154/6,154/12,154/13,155/6,156/5,159,
197/6,197/11,197/14,197/15,197/17,197/18,197/29,197/32,205 ,
208,209

# LAYOUT PLAN SHOWING BEFORE AMALGAMATIONS OF FOR KALEIDOSCOPE TOWNSHIP (41.90 HA)

OLD SURVEY NO
125/5, 126/2, 126/3, 126/4, 127/1,127/3,127/4,127/5,128/1,128/4,129/2,
129/5,131/3,132/1,132/2,133/1,133/2,133/3,134/1,135/1,135/3,136/1,136/3,
137/1+2,138/1,138/2,138/4,138/5,140,141/2,141/3,141/4,141/5,142/1,142/2,
142/6,142/7,143,144/1/2A,144/1/2B,144/2,144/3A,145/1,145/2,145/3,145/5,146/1,
146/2,146/3,146/5,146/6,147/2,147/3,148,149/1,150/1,150/2,150/3,150/4,150/5,150/6,
150/7,151/1,152/2,153/1,153/2,154/2,154/4,145/5/1,154/5/2,154/5/3,154/6,154/7,154/8,
154/9,154/10,154/11,154/15,155/1,155/2,155/4,155/5,155/6,155/7,156/1,156/2,156/3,156/4,
156/5,156/6,156/7,156/8,157,159,188/2,197/1,197/5,197/6,197/7,197/9,197/12,197/16,197/18,
197/21,197/23,197/24,197/26,197/27,197/28,197/29,197/30,197/32,198,199,200,201,128/3,
129/5,129/6,131/3,131/6,131/7,133/1,134/4,133/5,134/1,135/1,135/3,136/1,137/1+2,155/2,
156/2,156/8,197/8,197/24,197/27,200,

NEW SURVEY NO ADD FOR TOWNSHIP
S.NO-128/3,129/5,129/6,131/1,131/3,131/5,134/1,135/2,135/3,136/1,
137/1,140,141/1,141/2,141/5,143,146/1,146/6,147/3,148,149/2,
150/7,151/2,152/1,154/1,154/6,154/12,154/13,155/6,156/5,159,
197/6,197/11,197/14,197/15,197/17,197/18,197/29,197/32,205 ,
208,209

## LAND AREA TABLE AS PER LC1 &LC2

| S.No. | | PREVIOUS SANCTION AS PER PLU 12-07-24 | AREA IN HA. | TOTAL PROPOSED ITP | AREA IN HA. | AREA IN ACRES |
|---|---|---|---|---|---|---|
| 1 | PLOT AREA | 419034 | 41.9 | 477039 | 47.7 | 117.88 |
| 2 | AREA UNDER TOWNSHIP | 419034 | 41.9 | 477039 | 47.7 | 117.88 |
| 3 | TOTAL HILLSLOPE AREA | 66985.62 | 6.7 | 67977.47 | 6.8 | 16.80 |
| 4 | AREA UNDER DEVELOPMENT FOR CALCULATION OF FSI AND AMENITIES | 419034 | 41.9 | 409061.53 | 40.9 | 101.08 |
| 5 | BASIC FSI POTENTIAL OF TOWNSHIP | 419034 | 41.9 | 409061.53 | 40.9 | 101.08 |
| 6 | PREMIUM FSI POTENTIAL | 293323.8 | 29.3 | 409061.53 | 40.9 | 101.08 |
| 7 | Ancillary F.S.I | NA | NA | 490873.836 | 49.1 | 121.30 |
| 8 | TOTAL FSI | 712357.8 | 71.2 | 1308996.896 | 130.9 | 323.46 |

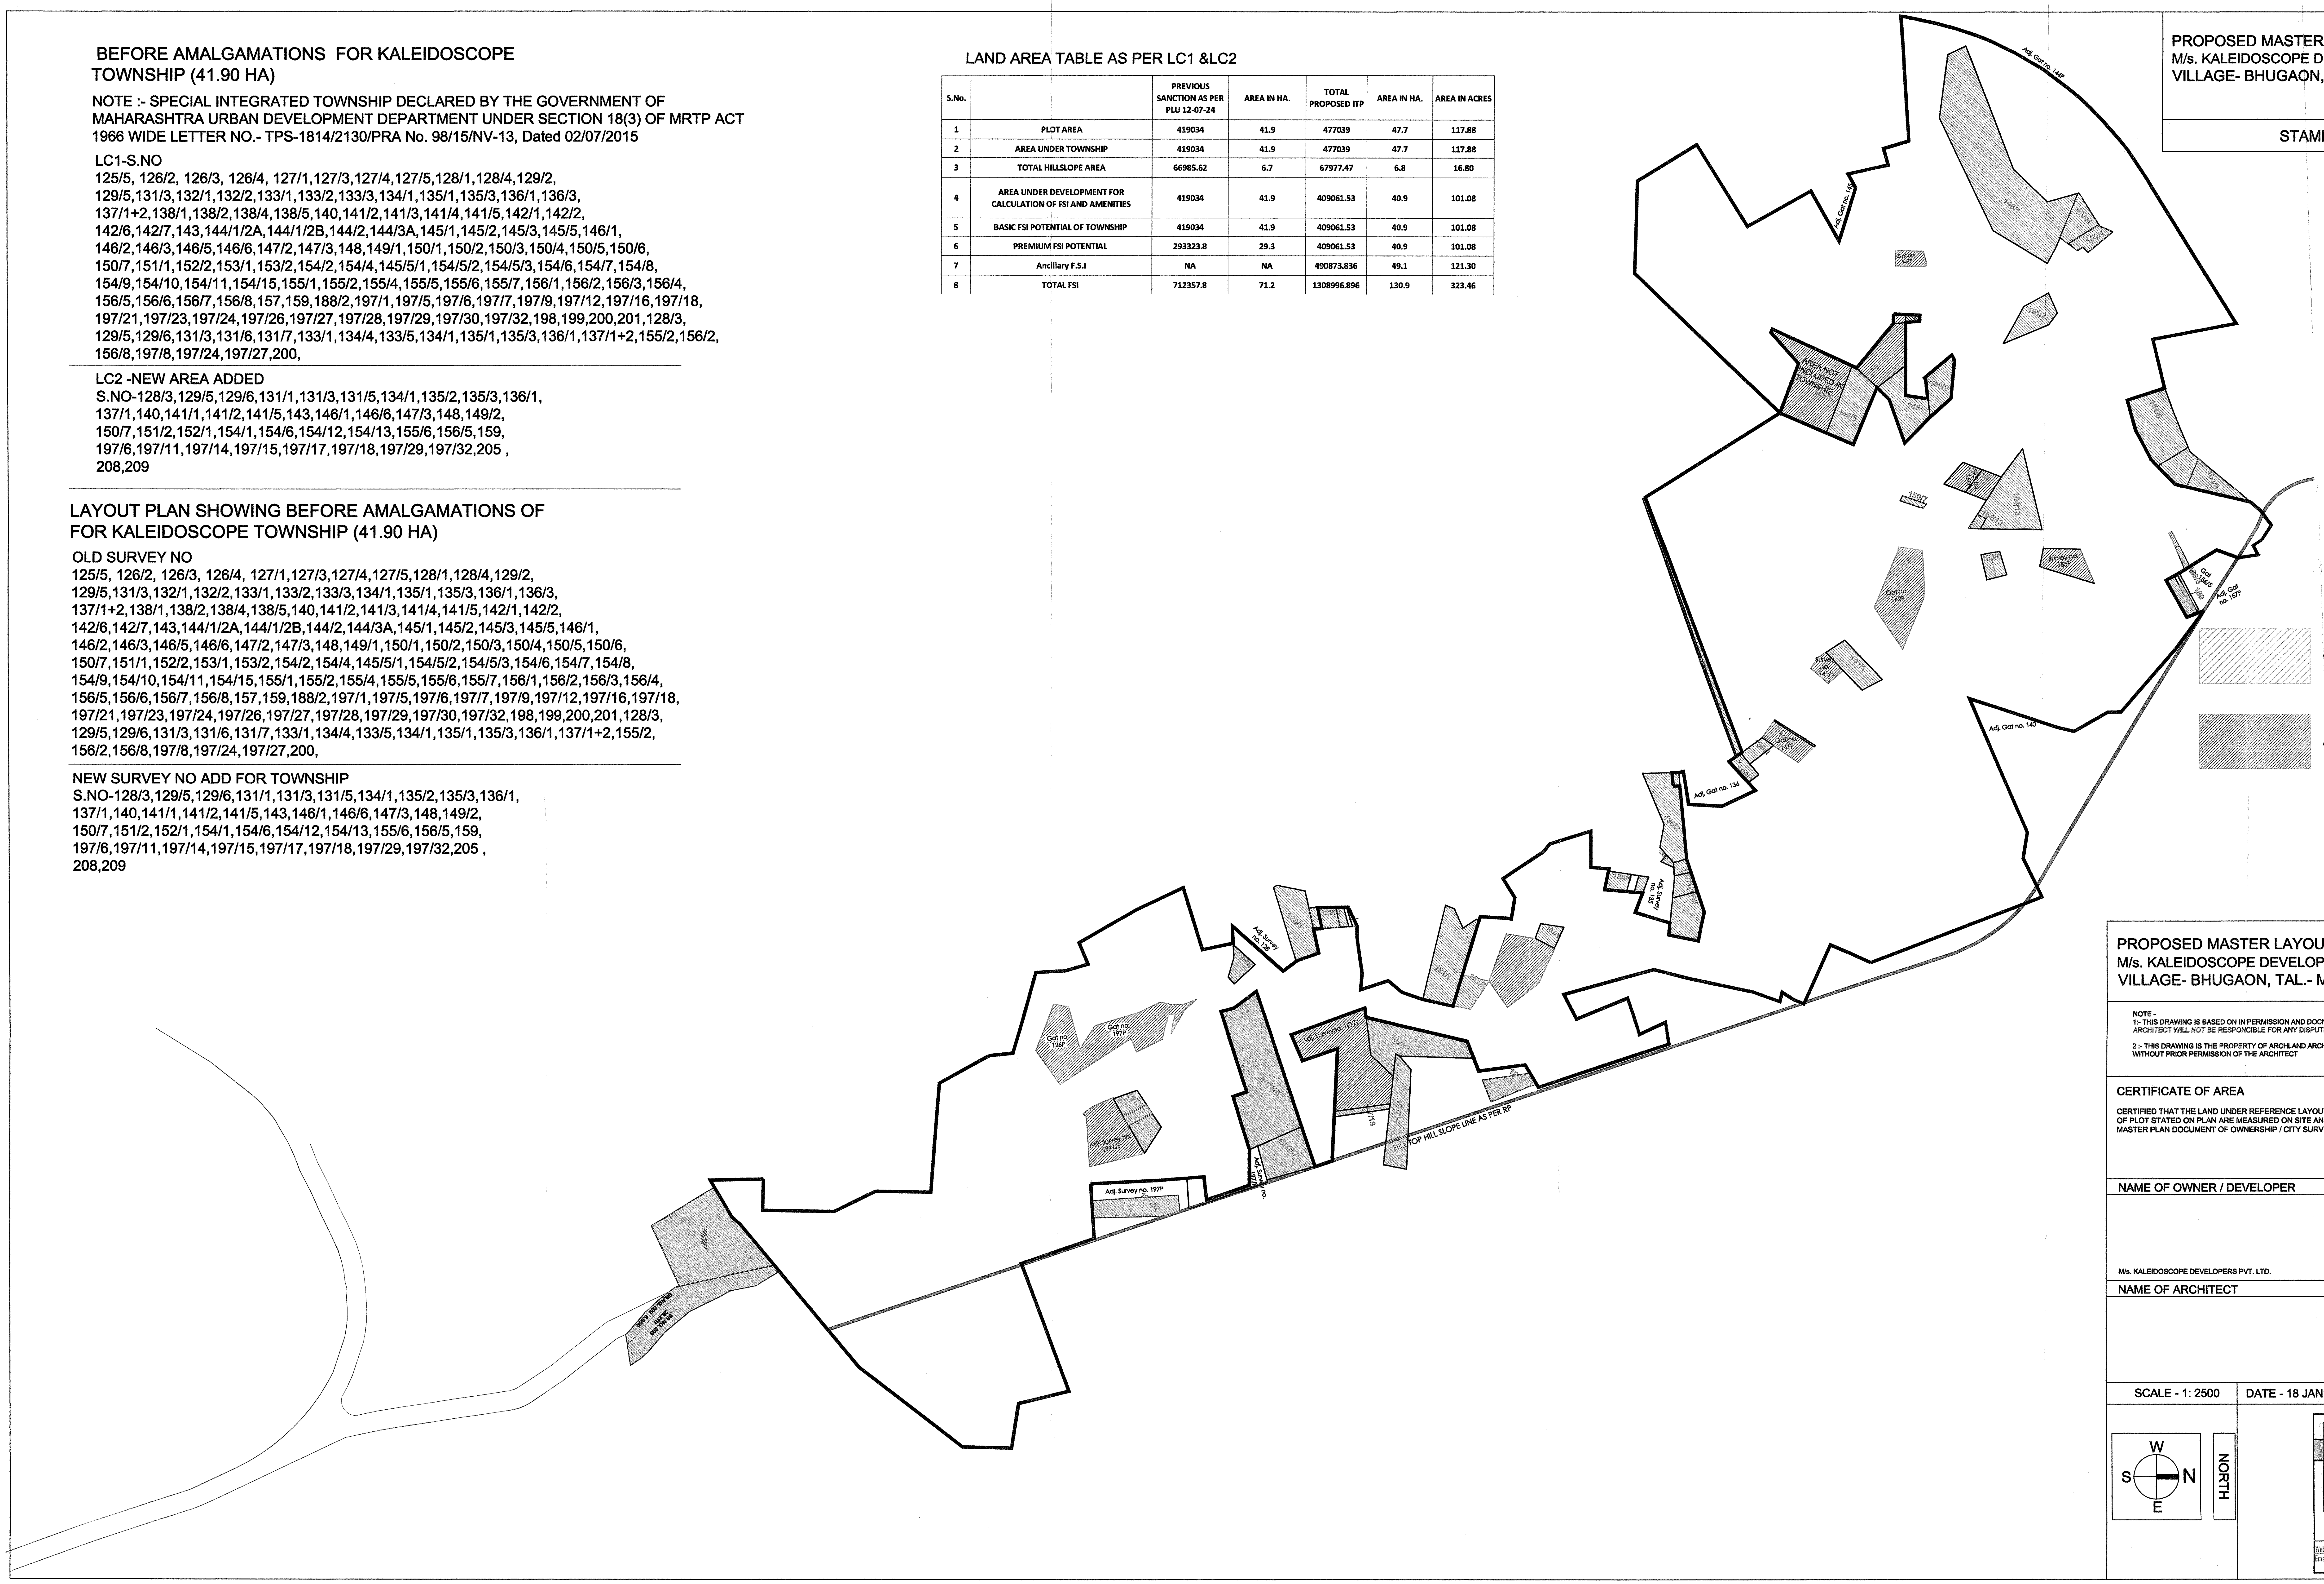

# PROPOSED MASTER LAYOUT PLAN (PLU) OF M/s. KALEIDOSCOPE DEVELOPERS PVT. LTD. VILLAGE- BHUGAON, TAL.-MULSHI, DIST.- PUNE

SHEET NO.
1
3

STAMP OF APPROVAL

Approved as amended in ____________
Subject to conditions mentioned in Annexure "A" of letter
No. BMU / C.R. No. २०१२/२४-२५ / Mouza भुगाव /
S. No. / G. No. / CTS No. १२५/५, १२६/२ व इतर
Dated :- २४/ ०१ /20२५

Deputy / Joint Metropolitan planner
Pune Metropolitan Regional Development Authority, Pune

# PROPOSED MASTER LAYOUT PLAN (PLU) OF M/s. KALEIDOSCOPE DEVELOPERS PVT. LTD. AT VILLAGE- BHUGAON, TAL.- MULSHI, DIST.- PUNE

NOTE -
1:- THIS DRAWING IS BASED ON IN PERMISSION AND DOCNUMENT PROVIDED BY OWNER/P.A.H. ARCHITECT WILL NOT BE RESPONCIBLE FOR ANY DISPUTE DIFFRENECES OR ANY LEGALITY OF THE OWNERSHIP.

2 :- THIS DRAWING IS THE PROPERTY OF ARCHLAND ARCHITECTS PVT. LTD. & THIS DRAWING SHOULD NOT BE COPIED OR USED WITHOUT PRIOR PERMISSION OF THE ARCHITECT

## CERTIFICATE OF AREA

CERTIFIED THAT THE LAND UNDER REFERENCE LAYOUT WAS SURVEYED BY ME AND THE DIMENSIONS OF THE SITES ETC. OF PLOT STATED ON PLAN ARE MEASURED ON SITE AND THE AREA SO WORKED OUT TALLIES WITH THE AREA STATED IN MASTER PLAN DOCUMENT OF OWNERSHIP / CITY SURVEY RECORS AND MEASUREMENT PLAN.

SIGNATURE OF ARCHITECT

NAME OF OWNER / DEVELOPER

M/s. KALEIDOSCOPE DEVELOPERS PVT. LTD.

MR. SARANG SUDHAKAR KALE
(OWNER/P.O.A.)

NAME OF ARCHITECT

Sambhaji Patil
CA-89-12155

For Archland

AR. SAMBHAJI PATIL

| SCALE - 1: 2500 | DATE - 18 JANUARY 2025 | PROJECT ARCHITECT - AR.ARCHANA |
|---|---|---|

W
S N
E
NORTH

ARCHLAND
Ar.Sambhaji Patil
CTSNo.1108,Final Plot No.487,Sub Plot No.4,8-Manasara,
III Floor,T.P.Scheme No.1,GaneshKhind Road,
Shivajinagar,Pune-400 116
Tel: (020)25665859 Mob:098230 57750
Web:www.archlandindia.com
Email:myarchland@gmail.com,arsambhajipatil@gmail.com
arsambhajipatil@archlandindia.com